A0—75

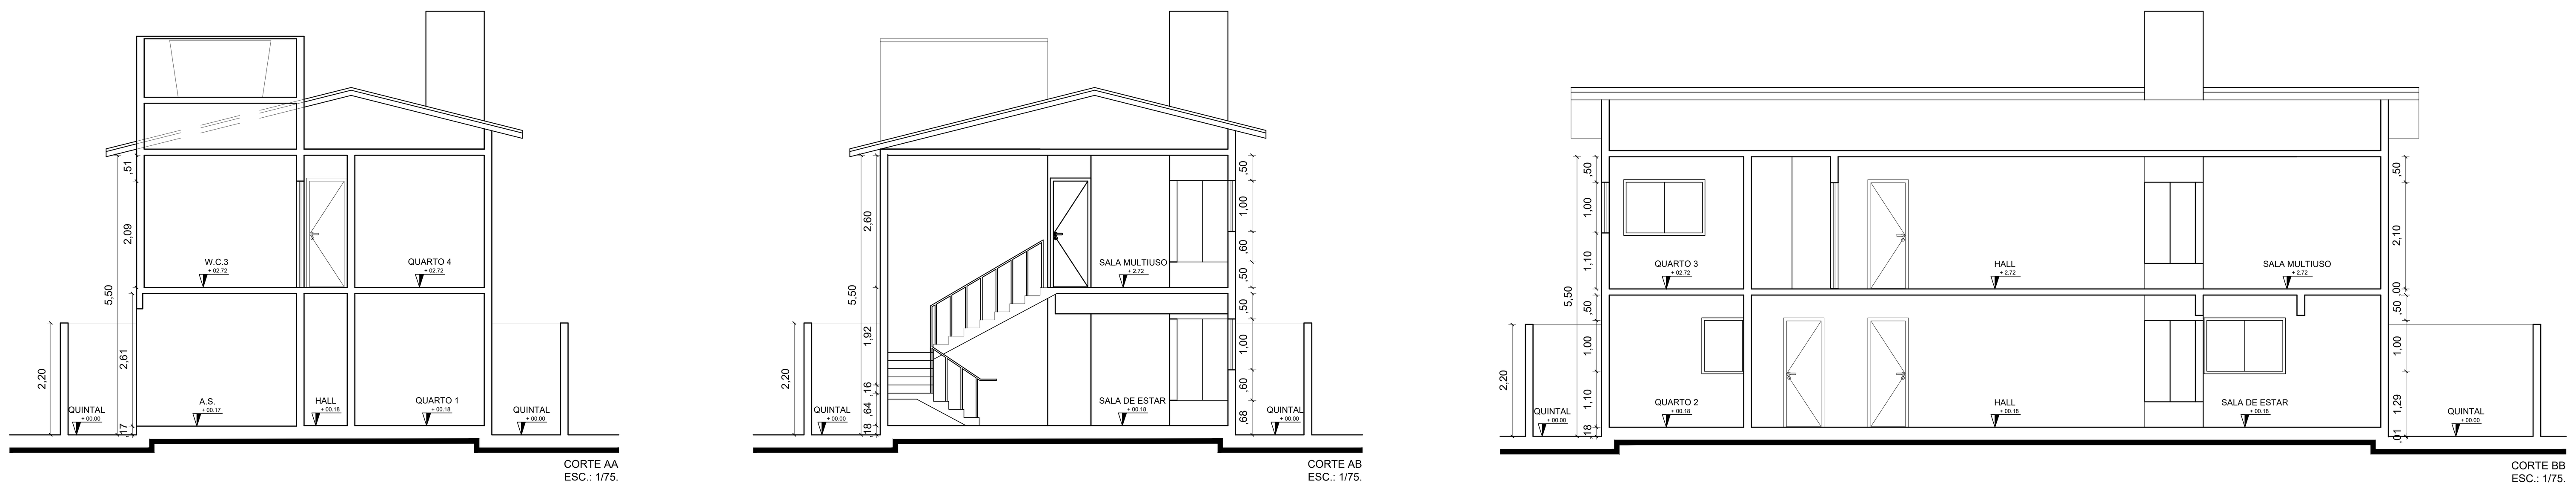

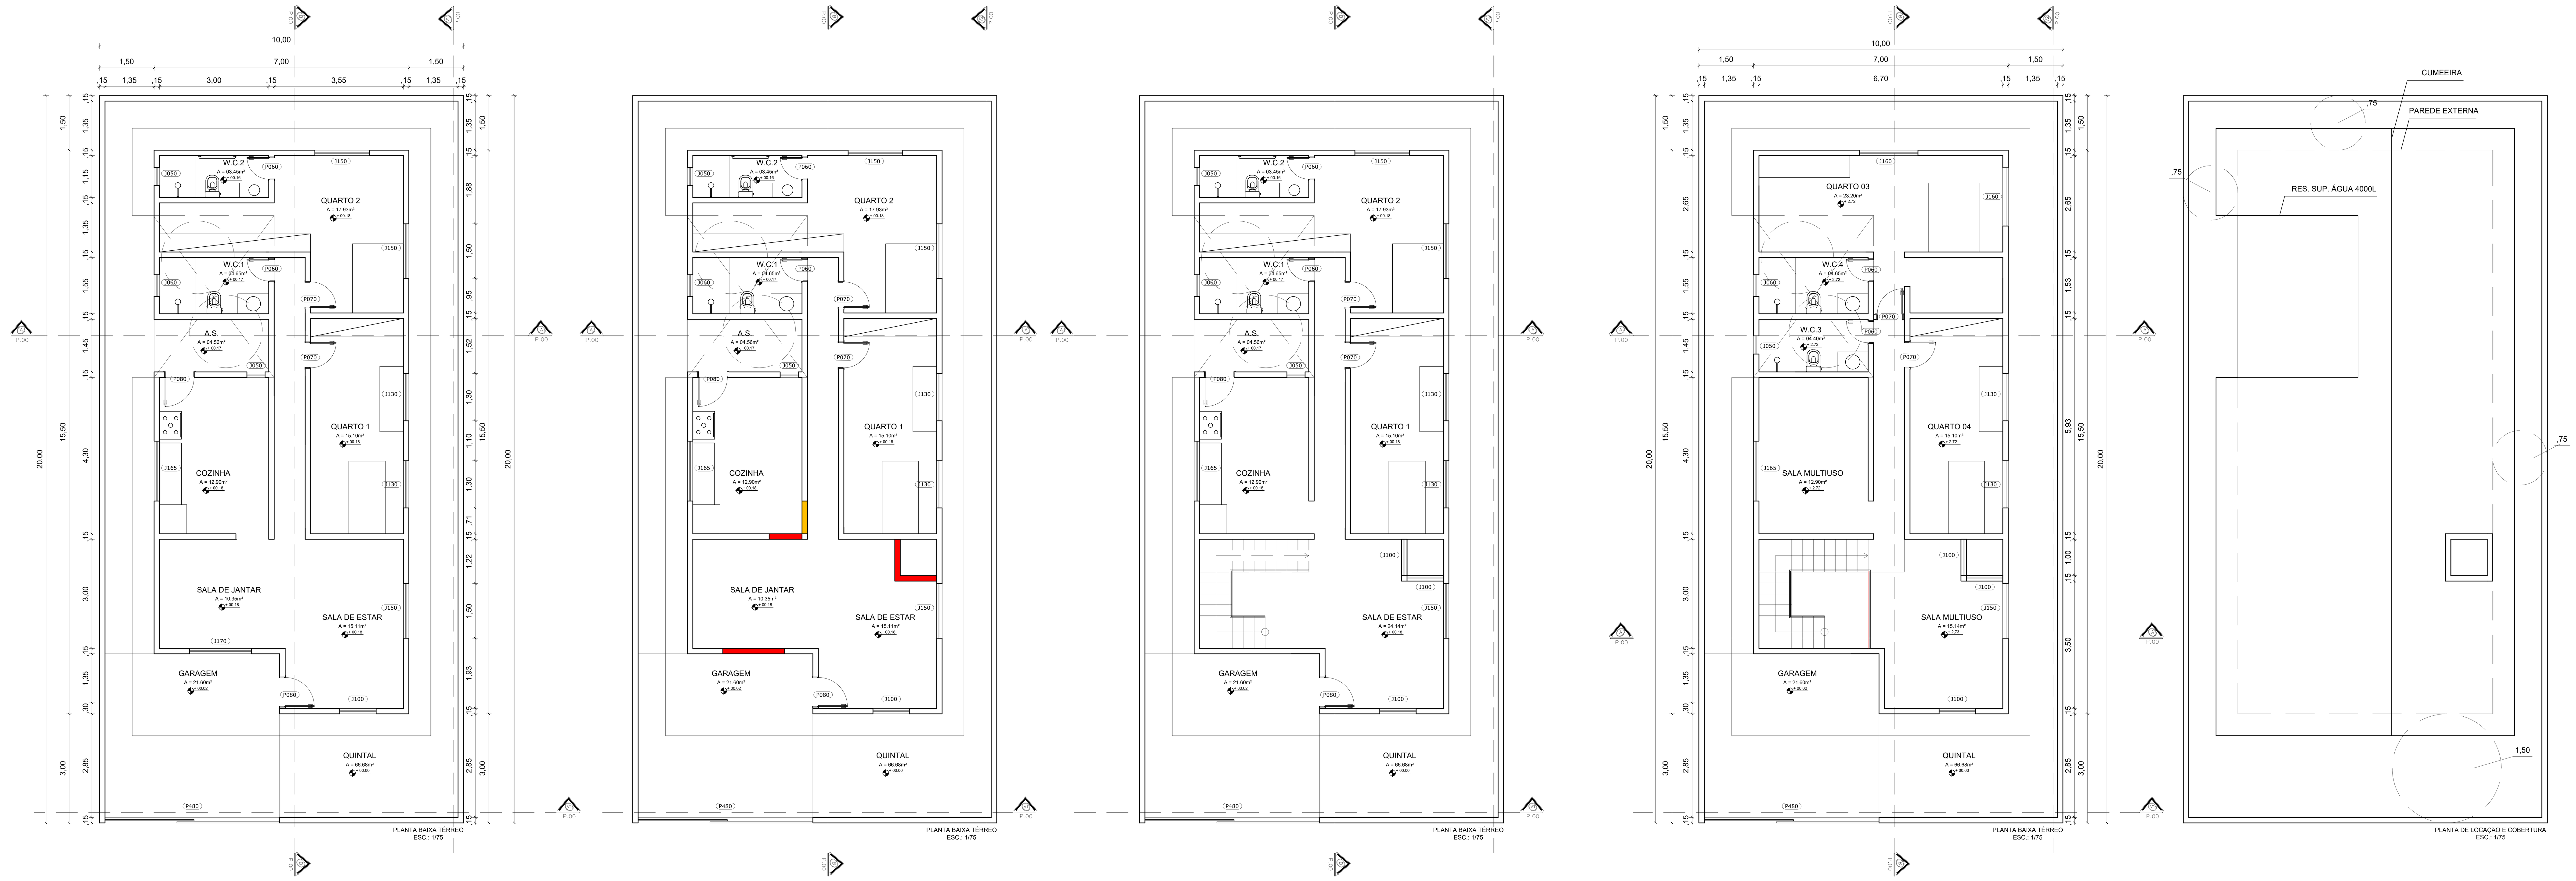

QUADRO DE ESQUADRIAS

CÓDIGO	DIMENSÕES			TIPO — MATERIAL	QUANT
	LARGURA	ALTURA	PEITORIL		
PORTAS					
P060	0,60	2,10	0,00	MADEIRA LAMINADA	04
P070	0,70	2,10	0,00	MADEIRA LAMINADA	04
P080	0,80	2,10	0,00	MADEIRA LAMINADA	02
JANELAS					
J050	0,50	2,10	1,60	ALUMÍNIO E VIDRO	03
J060	0,60	2,10	1,60	ALUMÍNIO E VIDRO	02
J100	1,00	2,10	1,10	ALUMÍNIO E VIDRO	01
J100	1,00	1,60	1,10	ALUMÍNIO E VIDRO	04
J130	1,30	2,10	1,10	ALUMÍNIO E VIDRO	04
J150	1,50	2,10	1,10	ALUMÍNIO E VIDRO	04
J160	1,60	2,10	1,10	ALUMÍNIO E VIDRO	02
J165	1,65	2,10	1,10	ALUMÍNIO E VIDRO	02
PORTÕES					
PP480	4,80	2,10	0,00	PORTÃO ALUMÍNIO	01

QUADRO DE ÁREAS (m^2)

1- A DO TERRENO:	200,00
2- A CONSTRUÍDA:	217,00
3- A ÚTIL:	192,75
4- A LAZER ÚTIL*:	000,00
5- A TÉCNICA ÚTIL*:	000,00
6- A PERMEÁVEL:	066,68
6- TAXA DE UTILIZAÇÃO DO TERRENO:	108,50

DISCENTE: CLÁUDIO DE SÁ NASCIMENTO FILHO E CARLOS HENRIQUE

DOCENTE: PABLO SOUSA

ATIVIDADE: REFORMA DO 1° PROJETO DE DESENHO ARQUITETÔNICO

CONTEÚDO: **PLANTA BAIXA, CORTES E FACHADAS.**

ETAPA: ANTEPROJETO

PRANCHA NÚMERO: **01/01**

DATA	DESENHO	ARQUIVO	ESCALA	REVISÃO
MÊS ANO	*.DWG	LOCAL NO DRIVE	1/75	